



Mauito and Pato's Residence / Mauricio Gallegos Arquitectos

Location: Merida, Mexico
Area: 270.0 mq
Project Year: 2015

La posizione dell'oggetto architettonico nel luogo risponde alla presenza di tre grandi alberi della regione: Manjack, Kapok e un Fishfuddle. Questi elementi motivano la disposizione di spazi e attività. Un asse compositivo parte dal Manjack e in esso si stabilisce l'accesso principale, dividendo la casa in area sociale e privata. Altro asse compositivo è la galleria di circolazione che attraversa e collega la residenza longitudinalmente. L'intersezione di questi assi si traduce in quattro aree: servizi, pubblico, sociale e privato. Lungo la galleria di circolazione sono posizionati lateralmente i blocchi di servizio. Lo spazio risultante tra questi è dove si trovano le aree viventi.

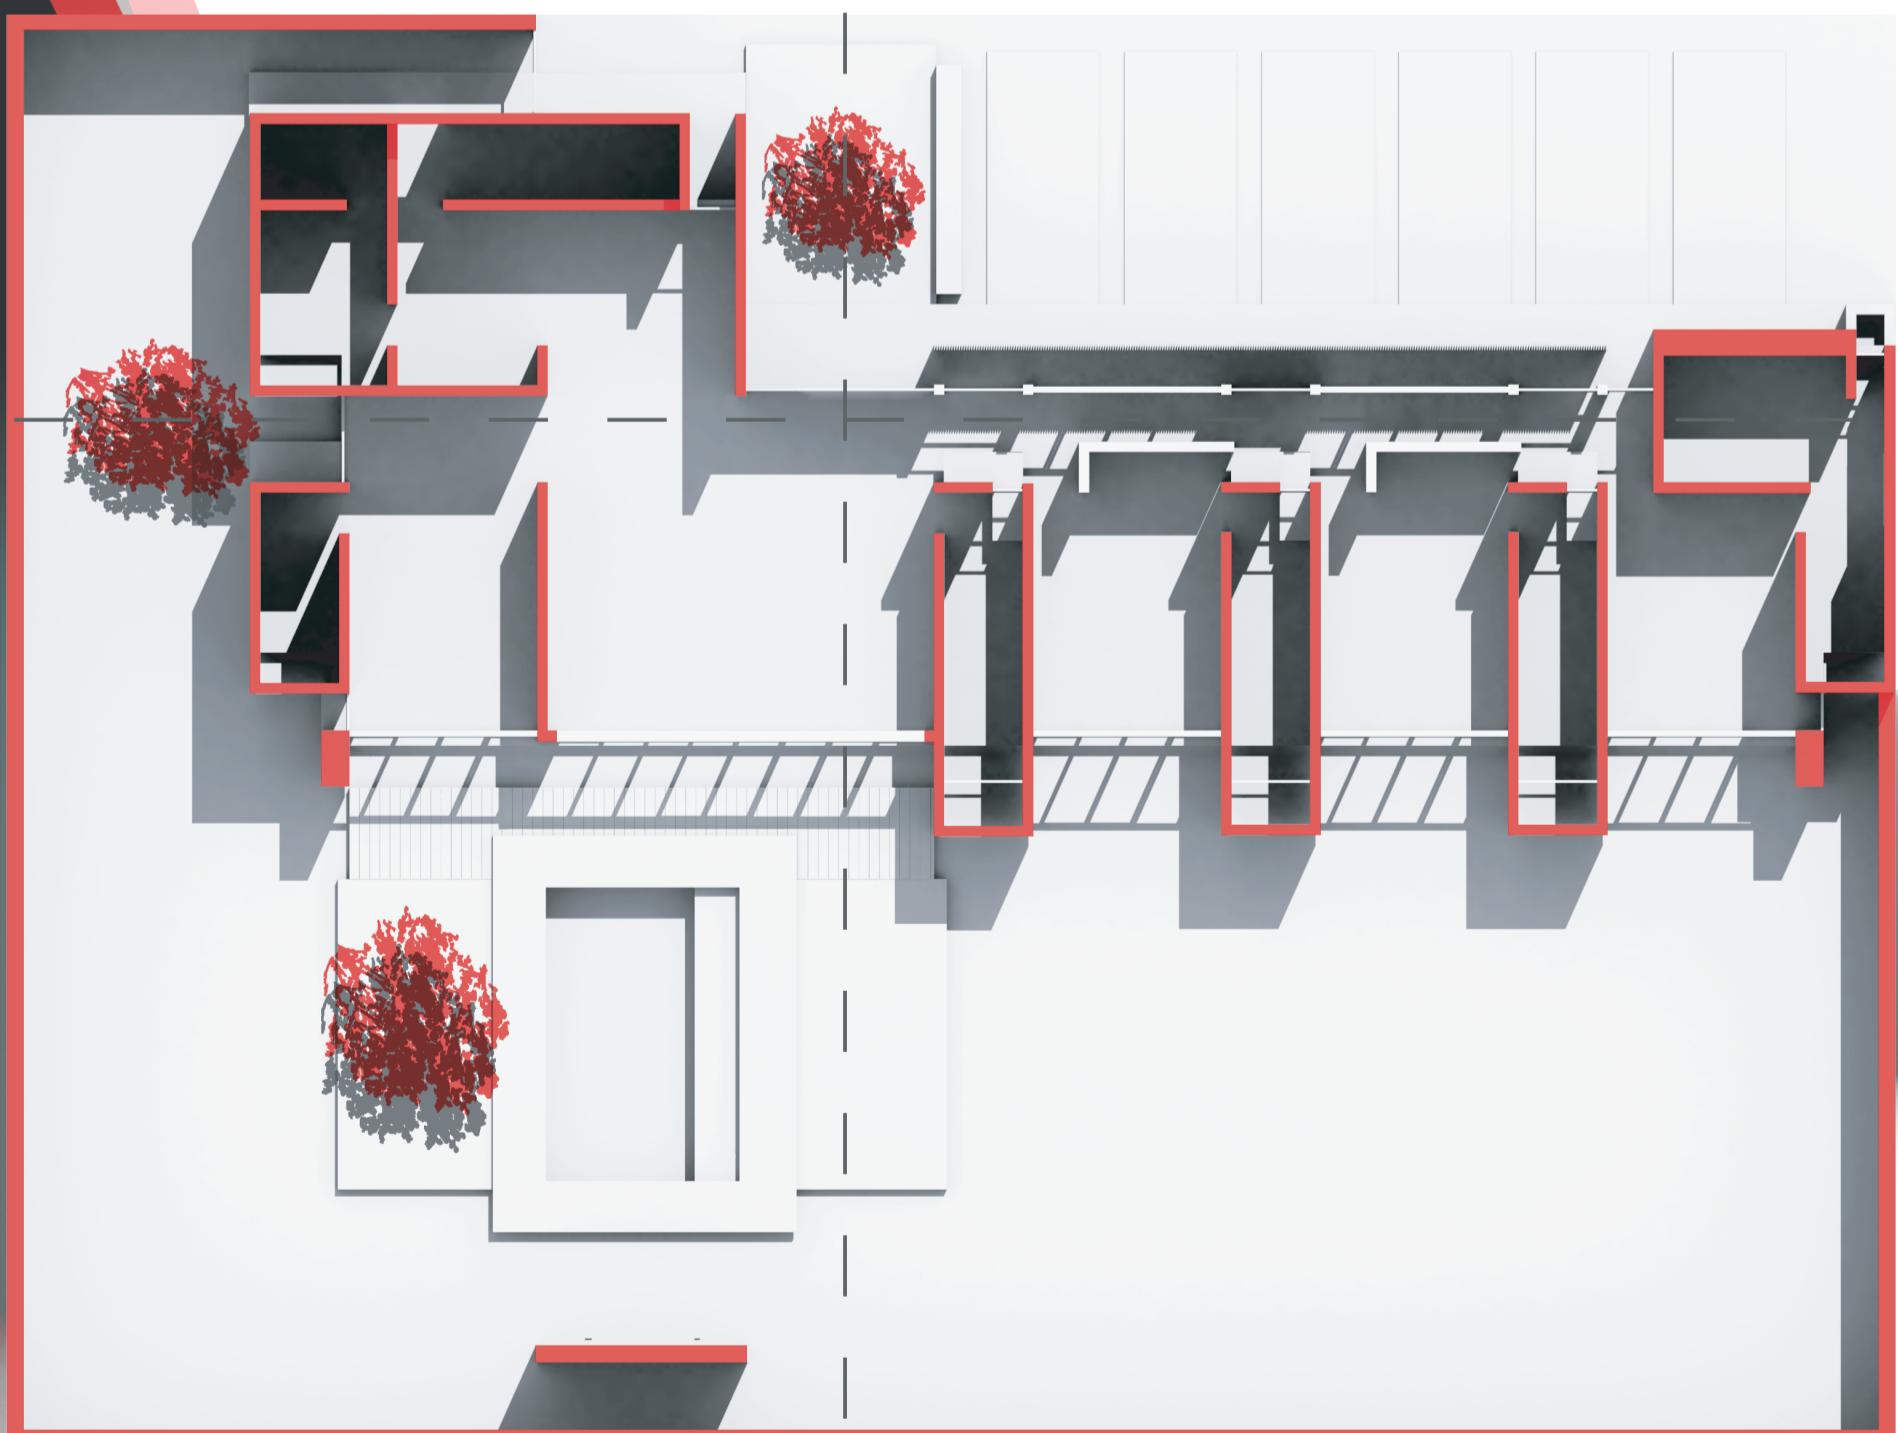

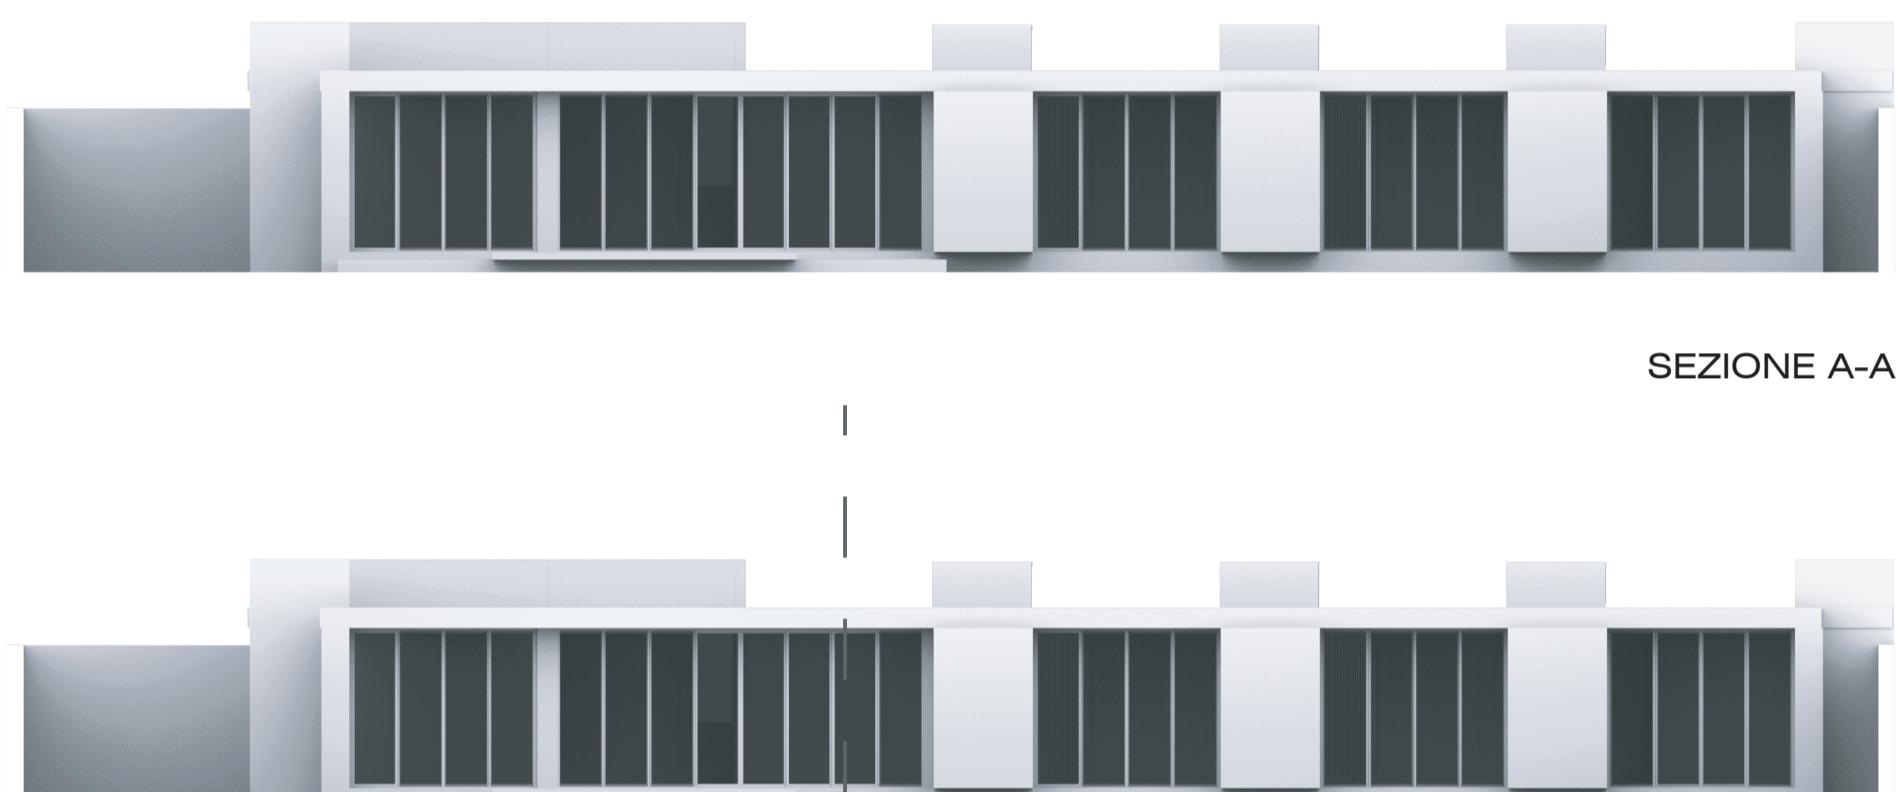

Mauito and Pato's Residence / Mauricio Gallegos Arquitectos

Location: Merida, Mexico
Area: 270.0 mq
Project Year: 2015


La posizione dell'oggetto architettonico nel luogo risponde alla presenza di tre grandi alberi della regione: Manjack, Kapok e un Fishfuddle. Questi elementi motivano la disposizione di spazi e attività. Un asse compositivo parte dal Manjack e in esso si stabilisce l'accesso principale, dividendo la casa in area sociale e privata. Altro asse compositivo è la galleria di circolazione che attraversa e collega la residenza longitudinalmente. L'intersezione di questi assi si traduce in quattro aree: servizi, pubblico, sociale e privato. Lungo la galleria di circolazione sono posizionati lateralmente i blocchi di servizio. Lo spazio risultante tra questi è dove si trovano le aree viventi.



SEZIONE A-A



SEZIONE B-B

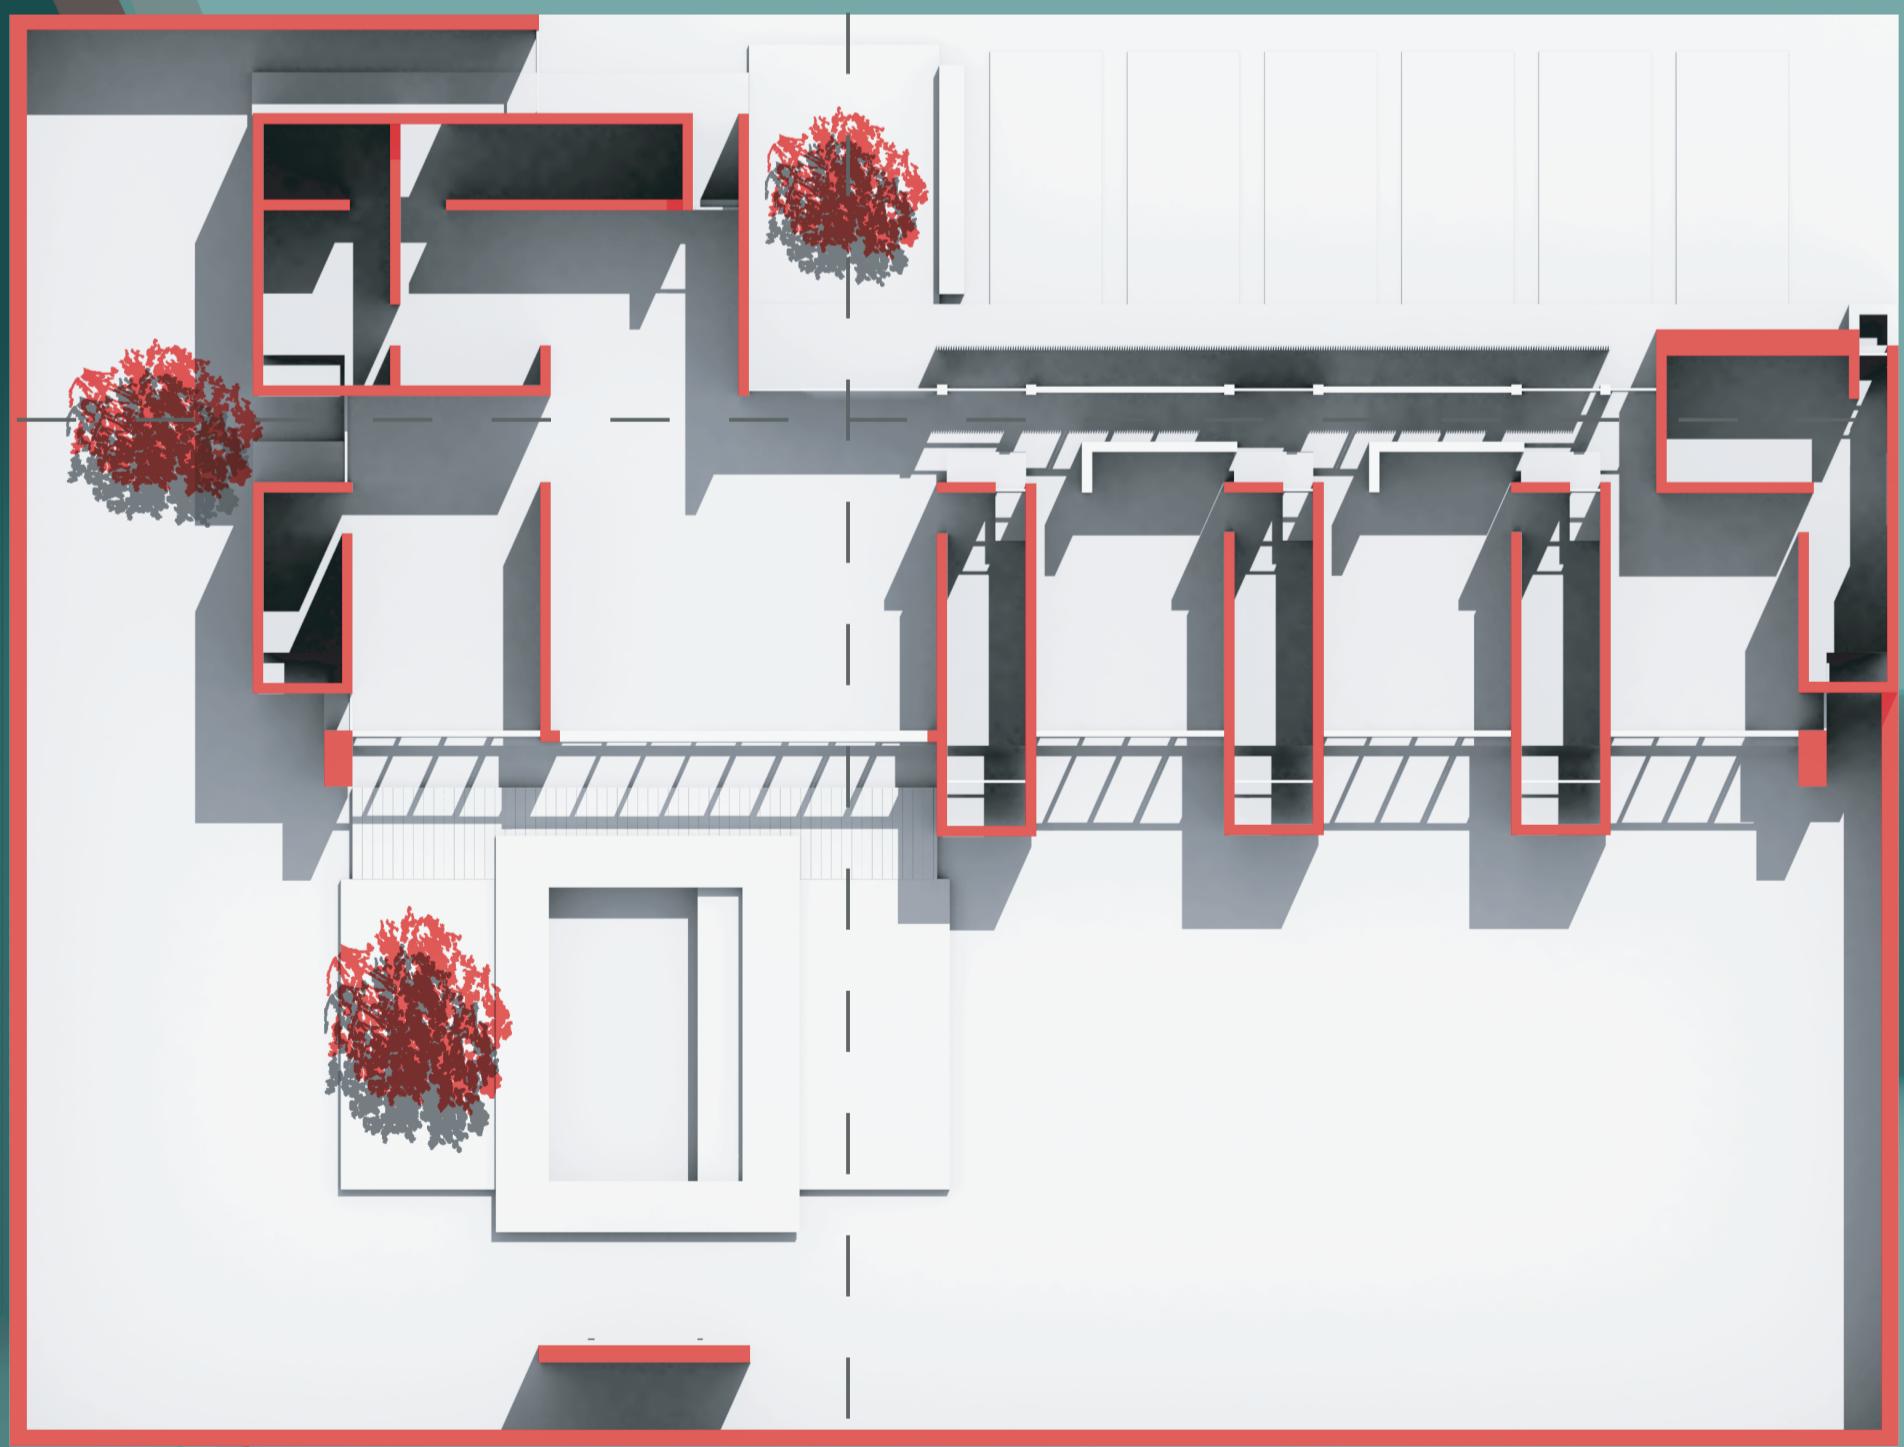

PLANIMETRIA